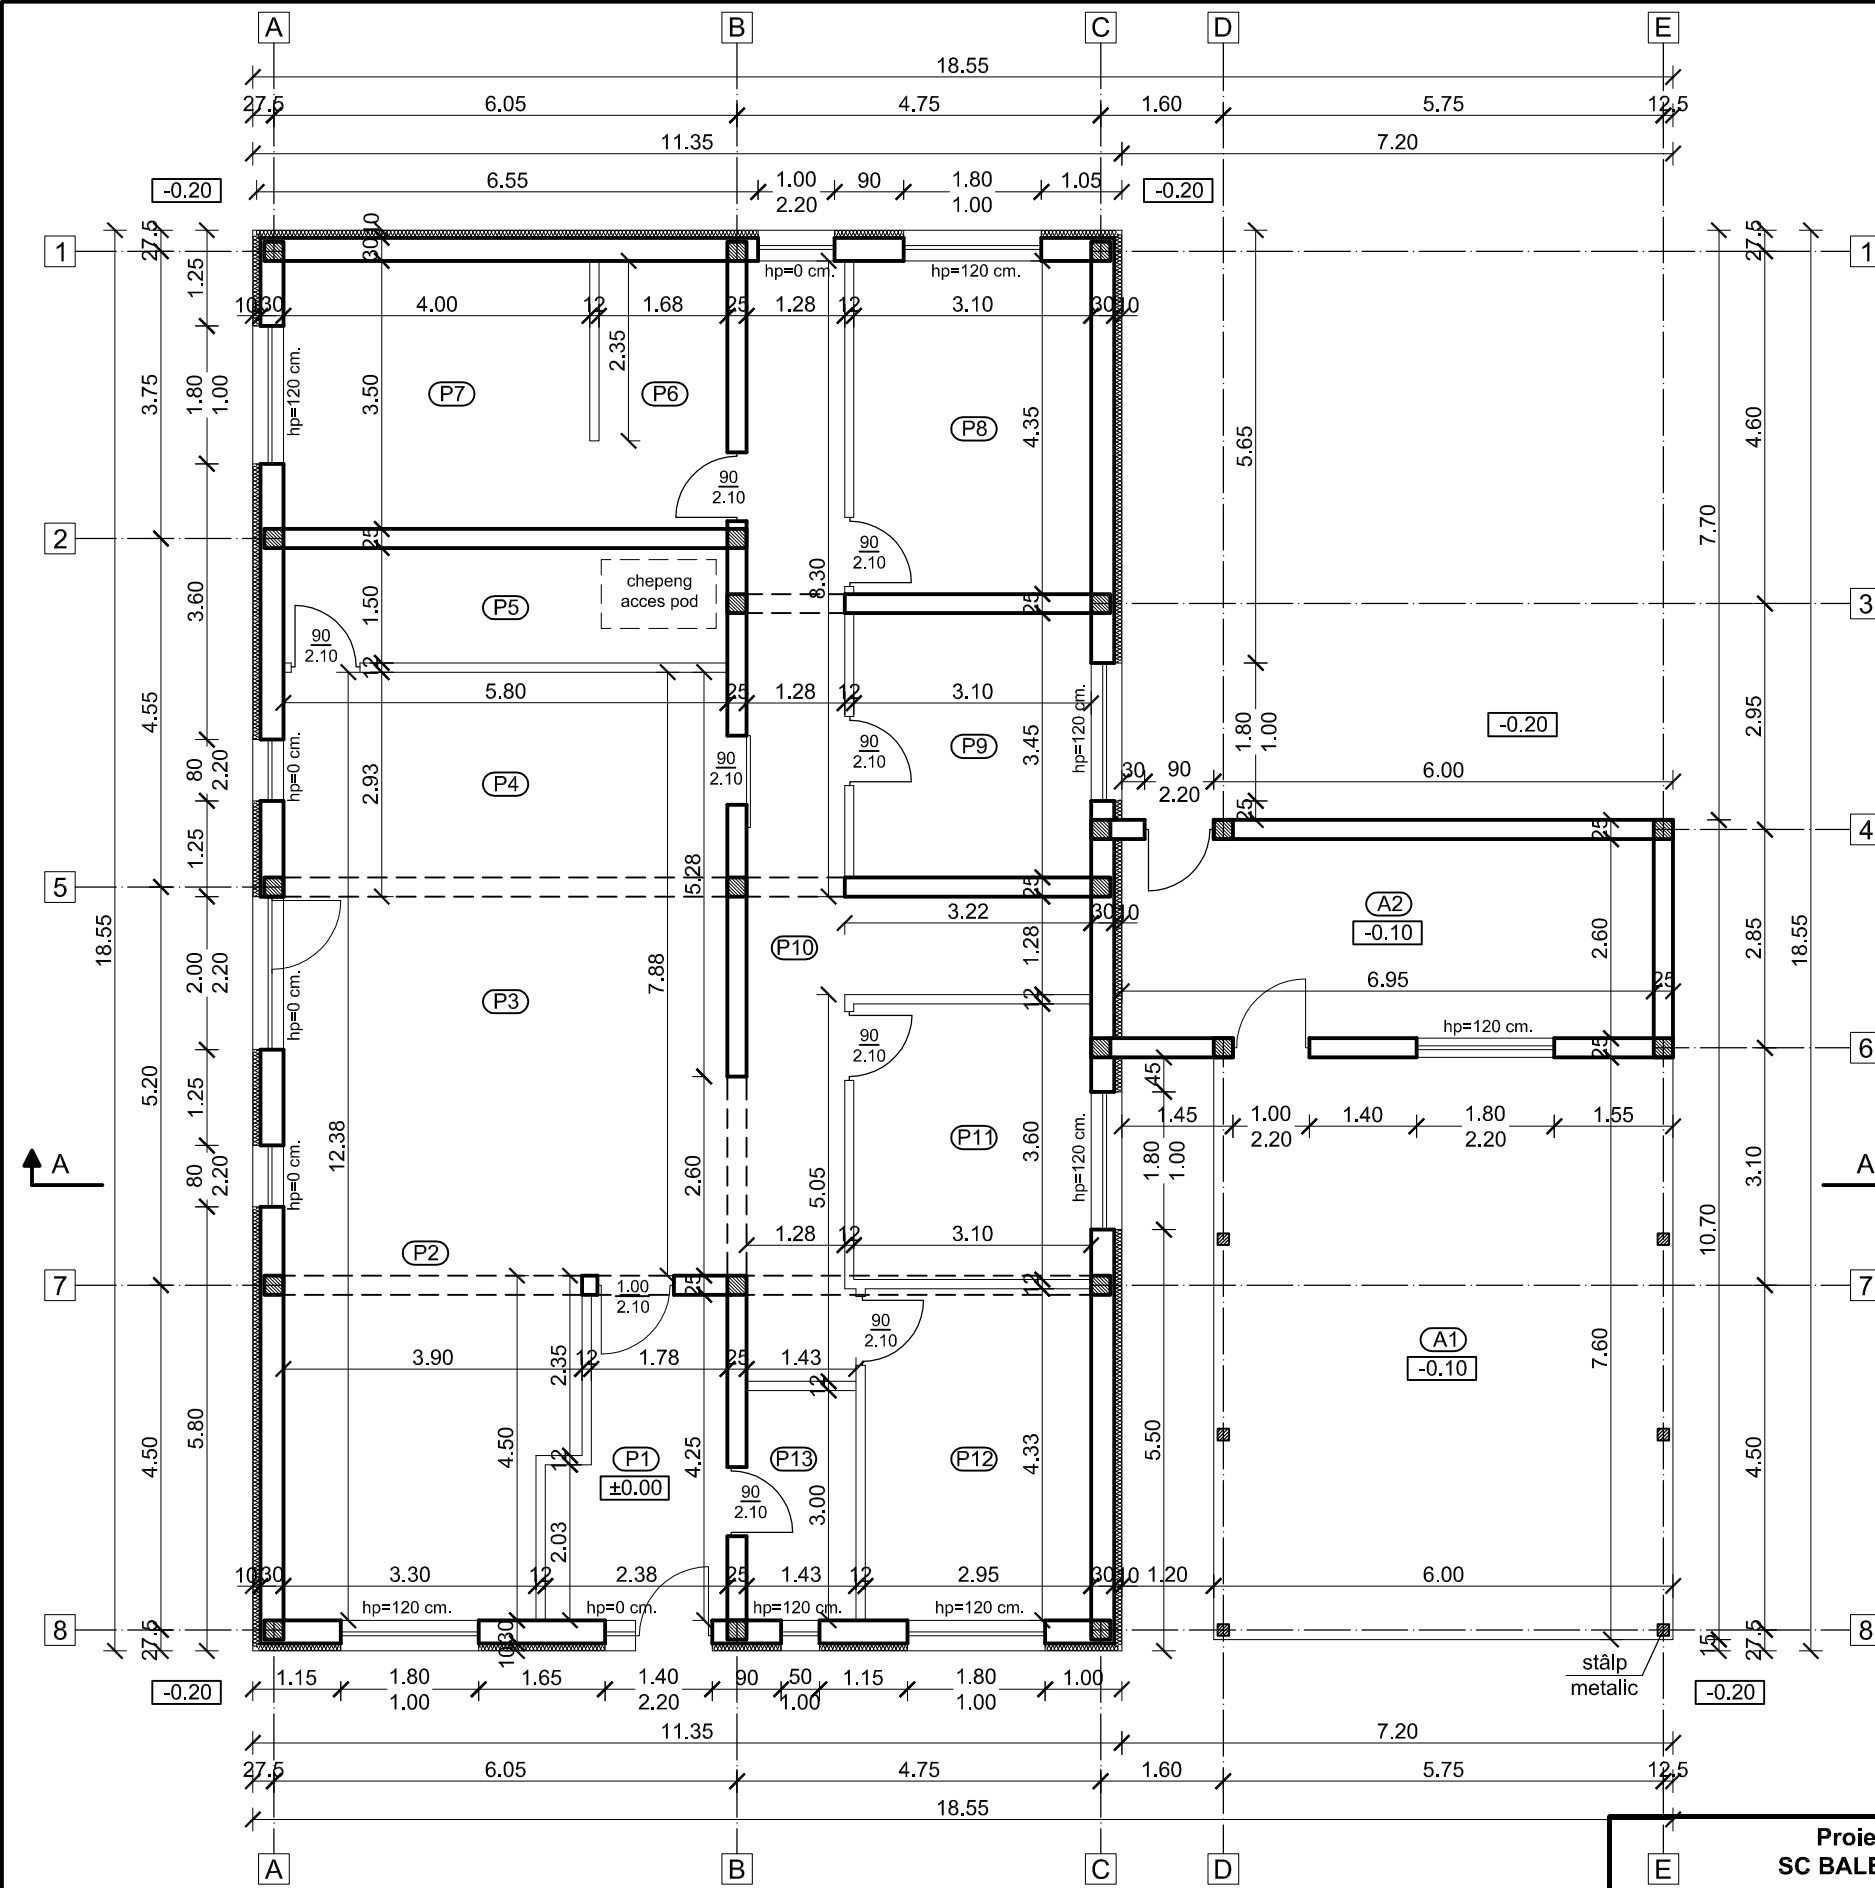


LEGENDĂ ÎNCĂPERI PARTER:

- CASĂ:**
 - (P1) Hol: S= 8.78 mp. pard. gresie
 - (P2) Living: S=31.34 mp. pard. parchet
 - (P3) Dining: S=13.63 mp. pard. parchet
 - (P4) Bucătărie: S=16.99 mp. pard. gresie
 - (P5) Cămară: S= 8.70 mp. pard. gresie
 - (P6) Dressing: S= 6.02 mp. pard. parchet
 - (P7) Dormitor: S=14.00 mp. pard. parchet
 - (P8) Dormitor: S=13.48 mp. pard. parchet
 - (P9) Baie: S=10.70 mp. pard. gresie
 - (P10) Hol: S=23.66 mp. pard. parchet
 - (P11) Birou: S=11.16 mp. pard. parchet
 - (P12) Dormitor: S=12.77 mp. pard. parchet
 - (P13) Baie: S= 4.29 mp. pard. gresie

S construită casă = 210.54 mp. (cu termoizolație)
S utilă casă = 175.52 mp.
- ANEXĂ:**
 - (A1) Copertină: S=45.60 mp. pard. gresogranit
 - (A2) Cameră tehnică: S=18.07 mp. pard. beton sclivisit

S construită anexă = 67.92 mp.
S utilă anexă = 18.07 mp.

S construită totală incintă (casă+anexă) = 278.46 mp.
S utilă totală incintă (casă+anexă) = 193.59 mp.

Proiectant general: SC BALEM PROIECT SRL ZALAU Proiectant de specialitate : SC I.G. PROIECT PLUS SRL ZALAU			Beneficiar	Denes Adorjan-Bela	
			Amplas.	com.Vârșolț, sat. Vârșolț, nr. 73/A, jud. Sălaj	
			Proiect	Construire locuință unifamilială parter, anexă gospodărească parter	
Șef proiect	Ing. Balint Eموke		Scara 1:100	PLAN PARTER	Proiect nr. 34/2026
Arhitectură	carh. Galvacsy Laszlo				Faza D.T.A.C.
Rezistență	ing. Balint Eموke		2026		Planșa A03