


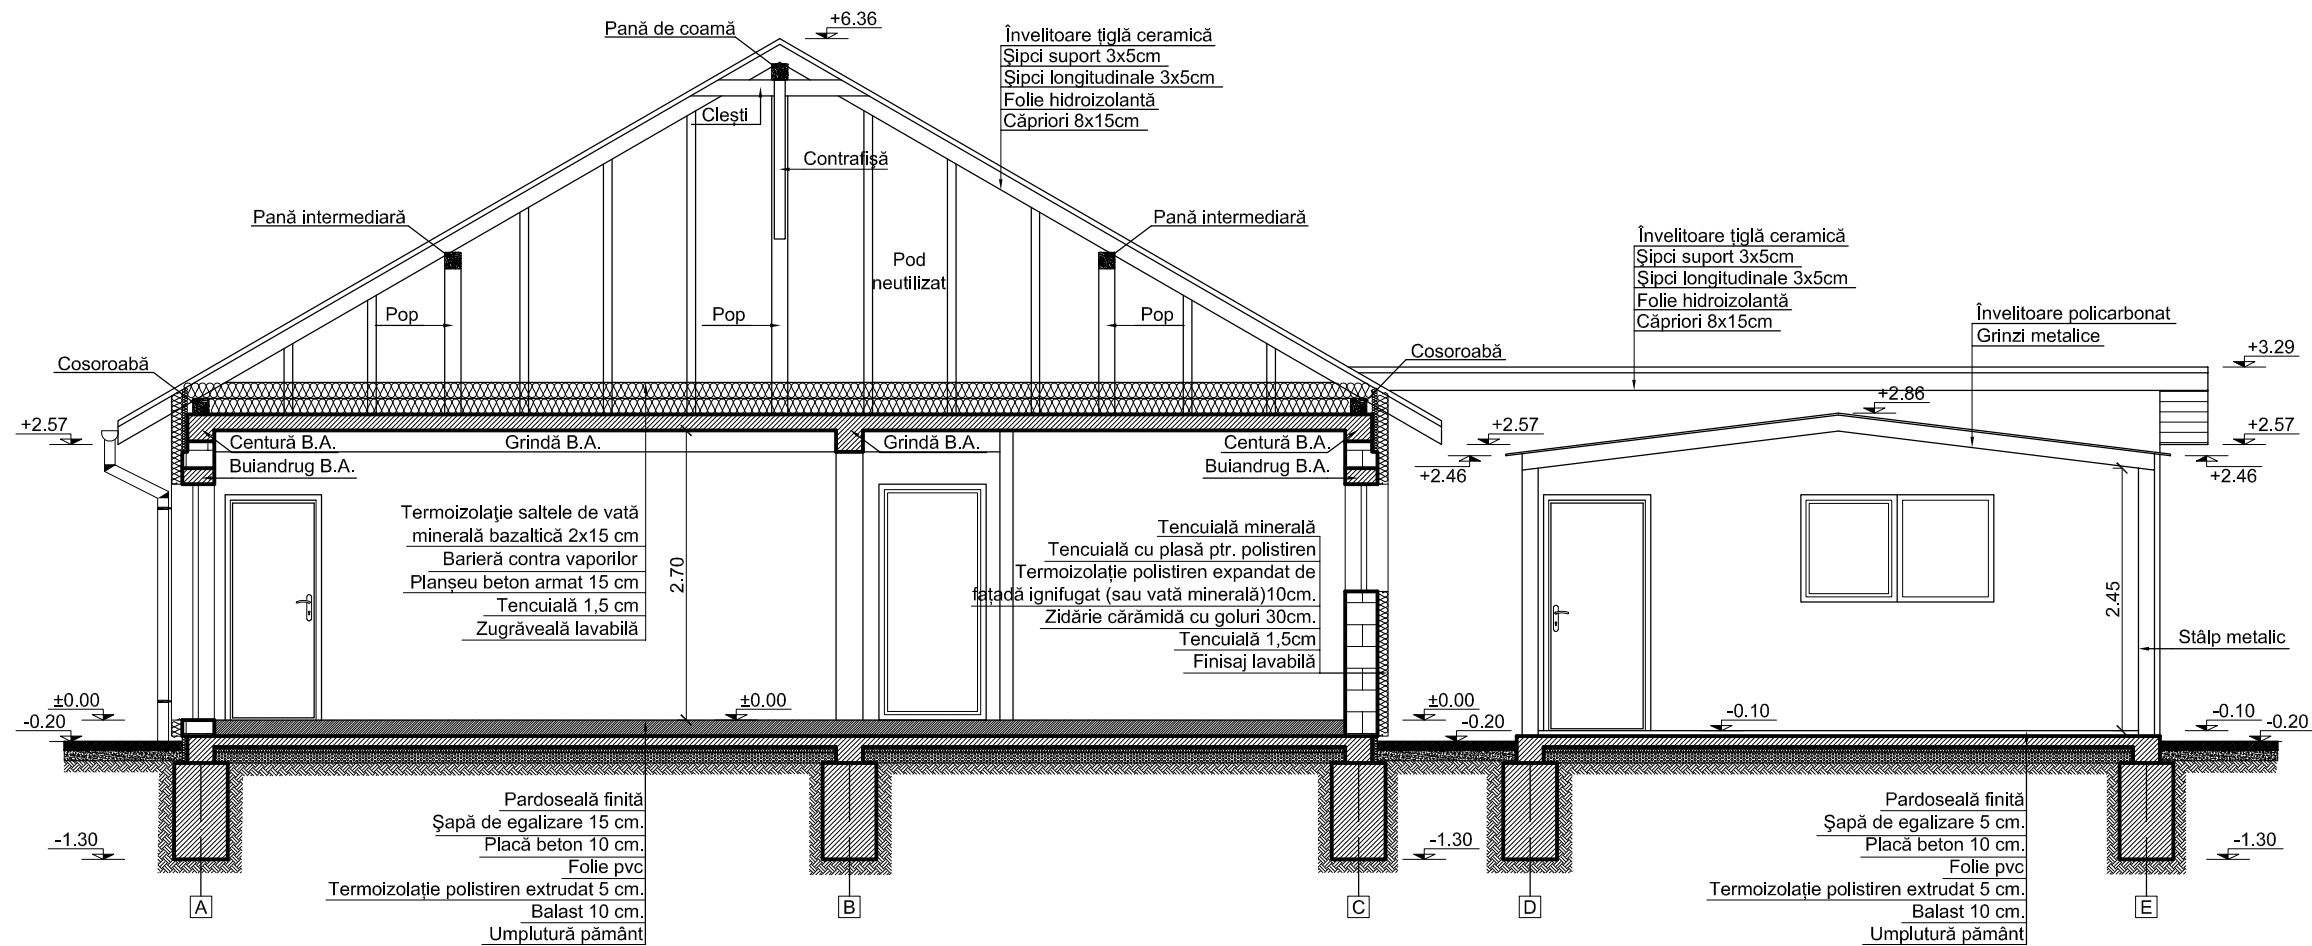

Proiectant general: SC BALEM PROIECT SRL ZALAU Proiectant de specialitate : SC I.G. PROIECT PLUS SRL ZALAU			Beneficiar	Denes Adorjan-Bela	
			Amplas.	com.Vârșolț, sat. Vârșolț, nr. 73/A, jud. Sălaj	
			Proiect	Construire locuință unifamilială parter, anexă gospodărească parter	
Șef proiect	ing. Balint Eموke		Scara 1:50	SECTIUNEA A-A	Proiect nr. 34/2026
Arhitectură	carh. Galvacsy Laszlo				Faza D.T.A.C.
Rezistență	ing. Balint Eموke		2026		Planșa A05